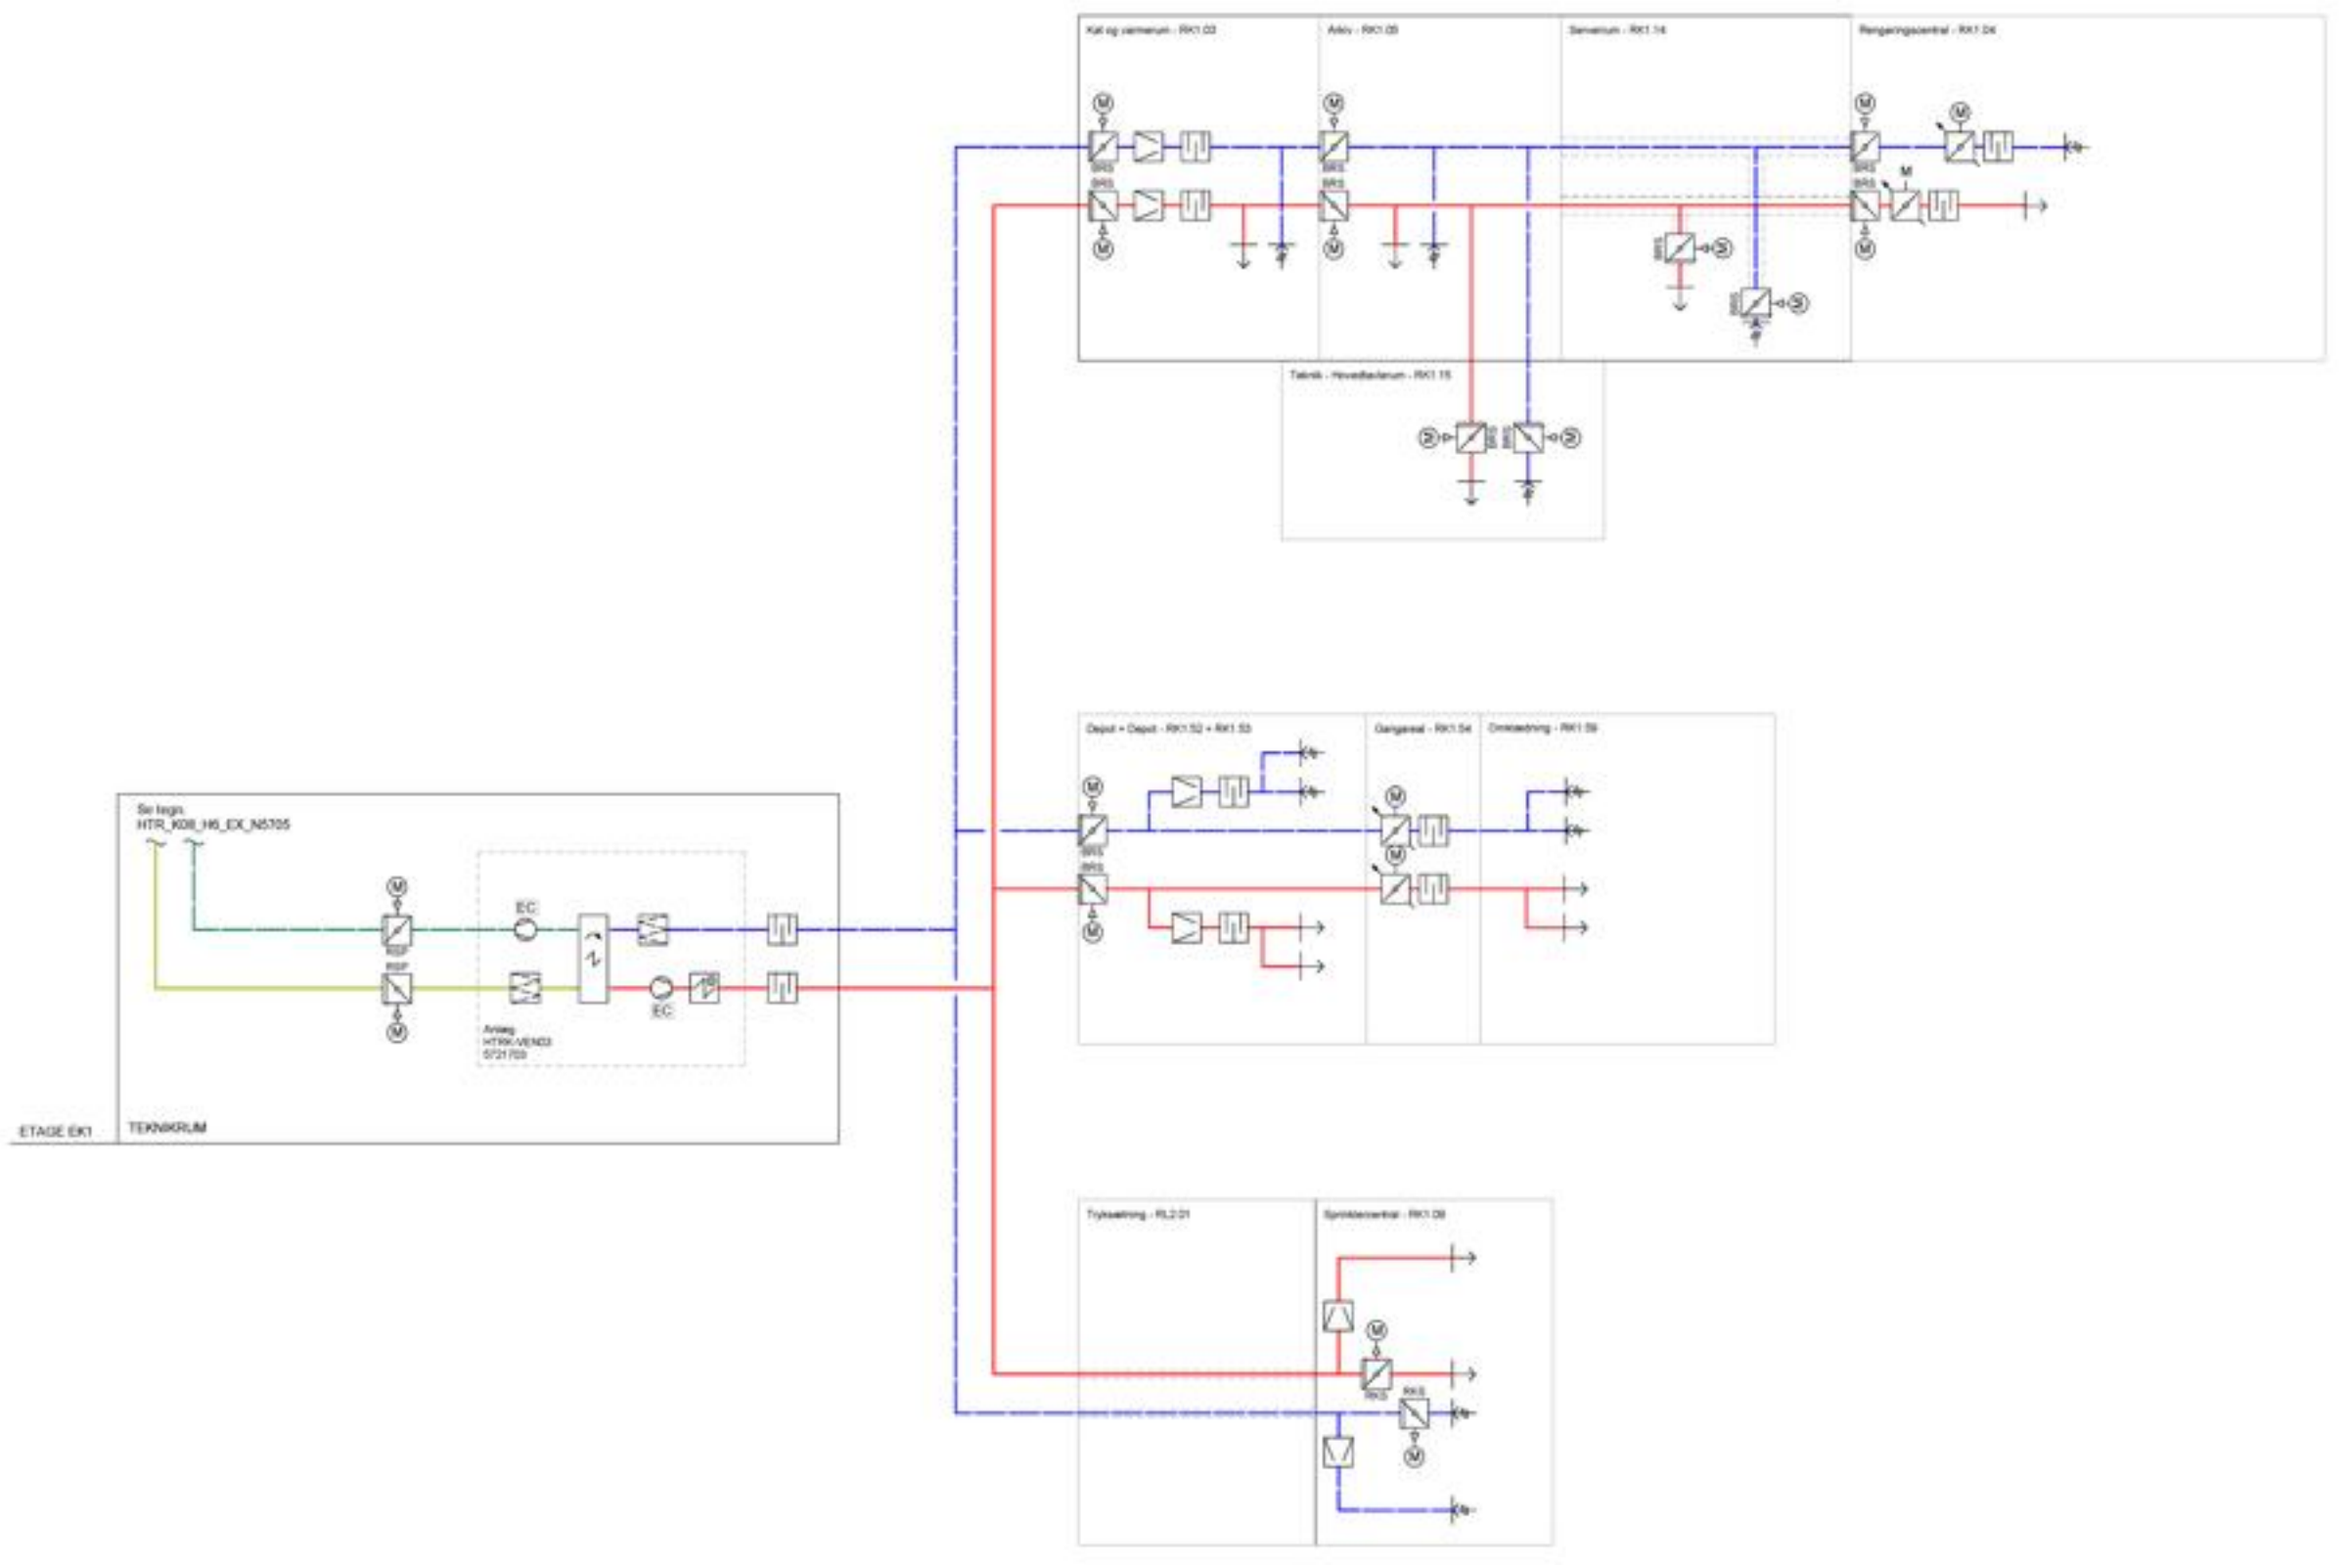
Kat og varmerum - RK1.03
Arkiv - RK1.05
Serverrum - RK1.14
Rengøringscentral - RK1.04
Teknik - Hovedtekrum - RK1.15
Depot + Depot - RK1.52 + RK1.53
Gangareal - RK1.54
Omklædning - RK1.59
Tryksætning - RL2.01
Sprinklercentral - RK1.09
Se tegn
HTR_K08_H6_EX_N5705
EC
EC
Anlæg
HTRK-VEN03
5721703
ETAGE EK1
TEKNIKRUM